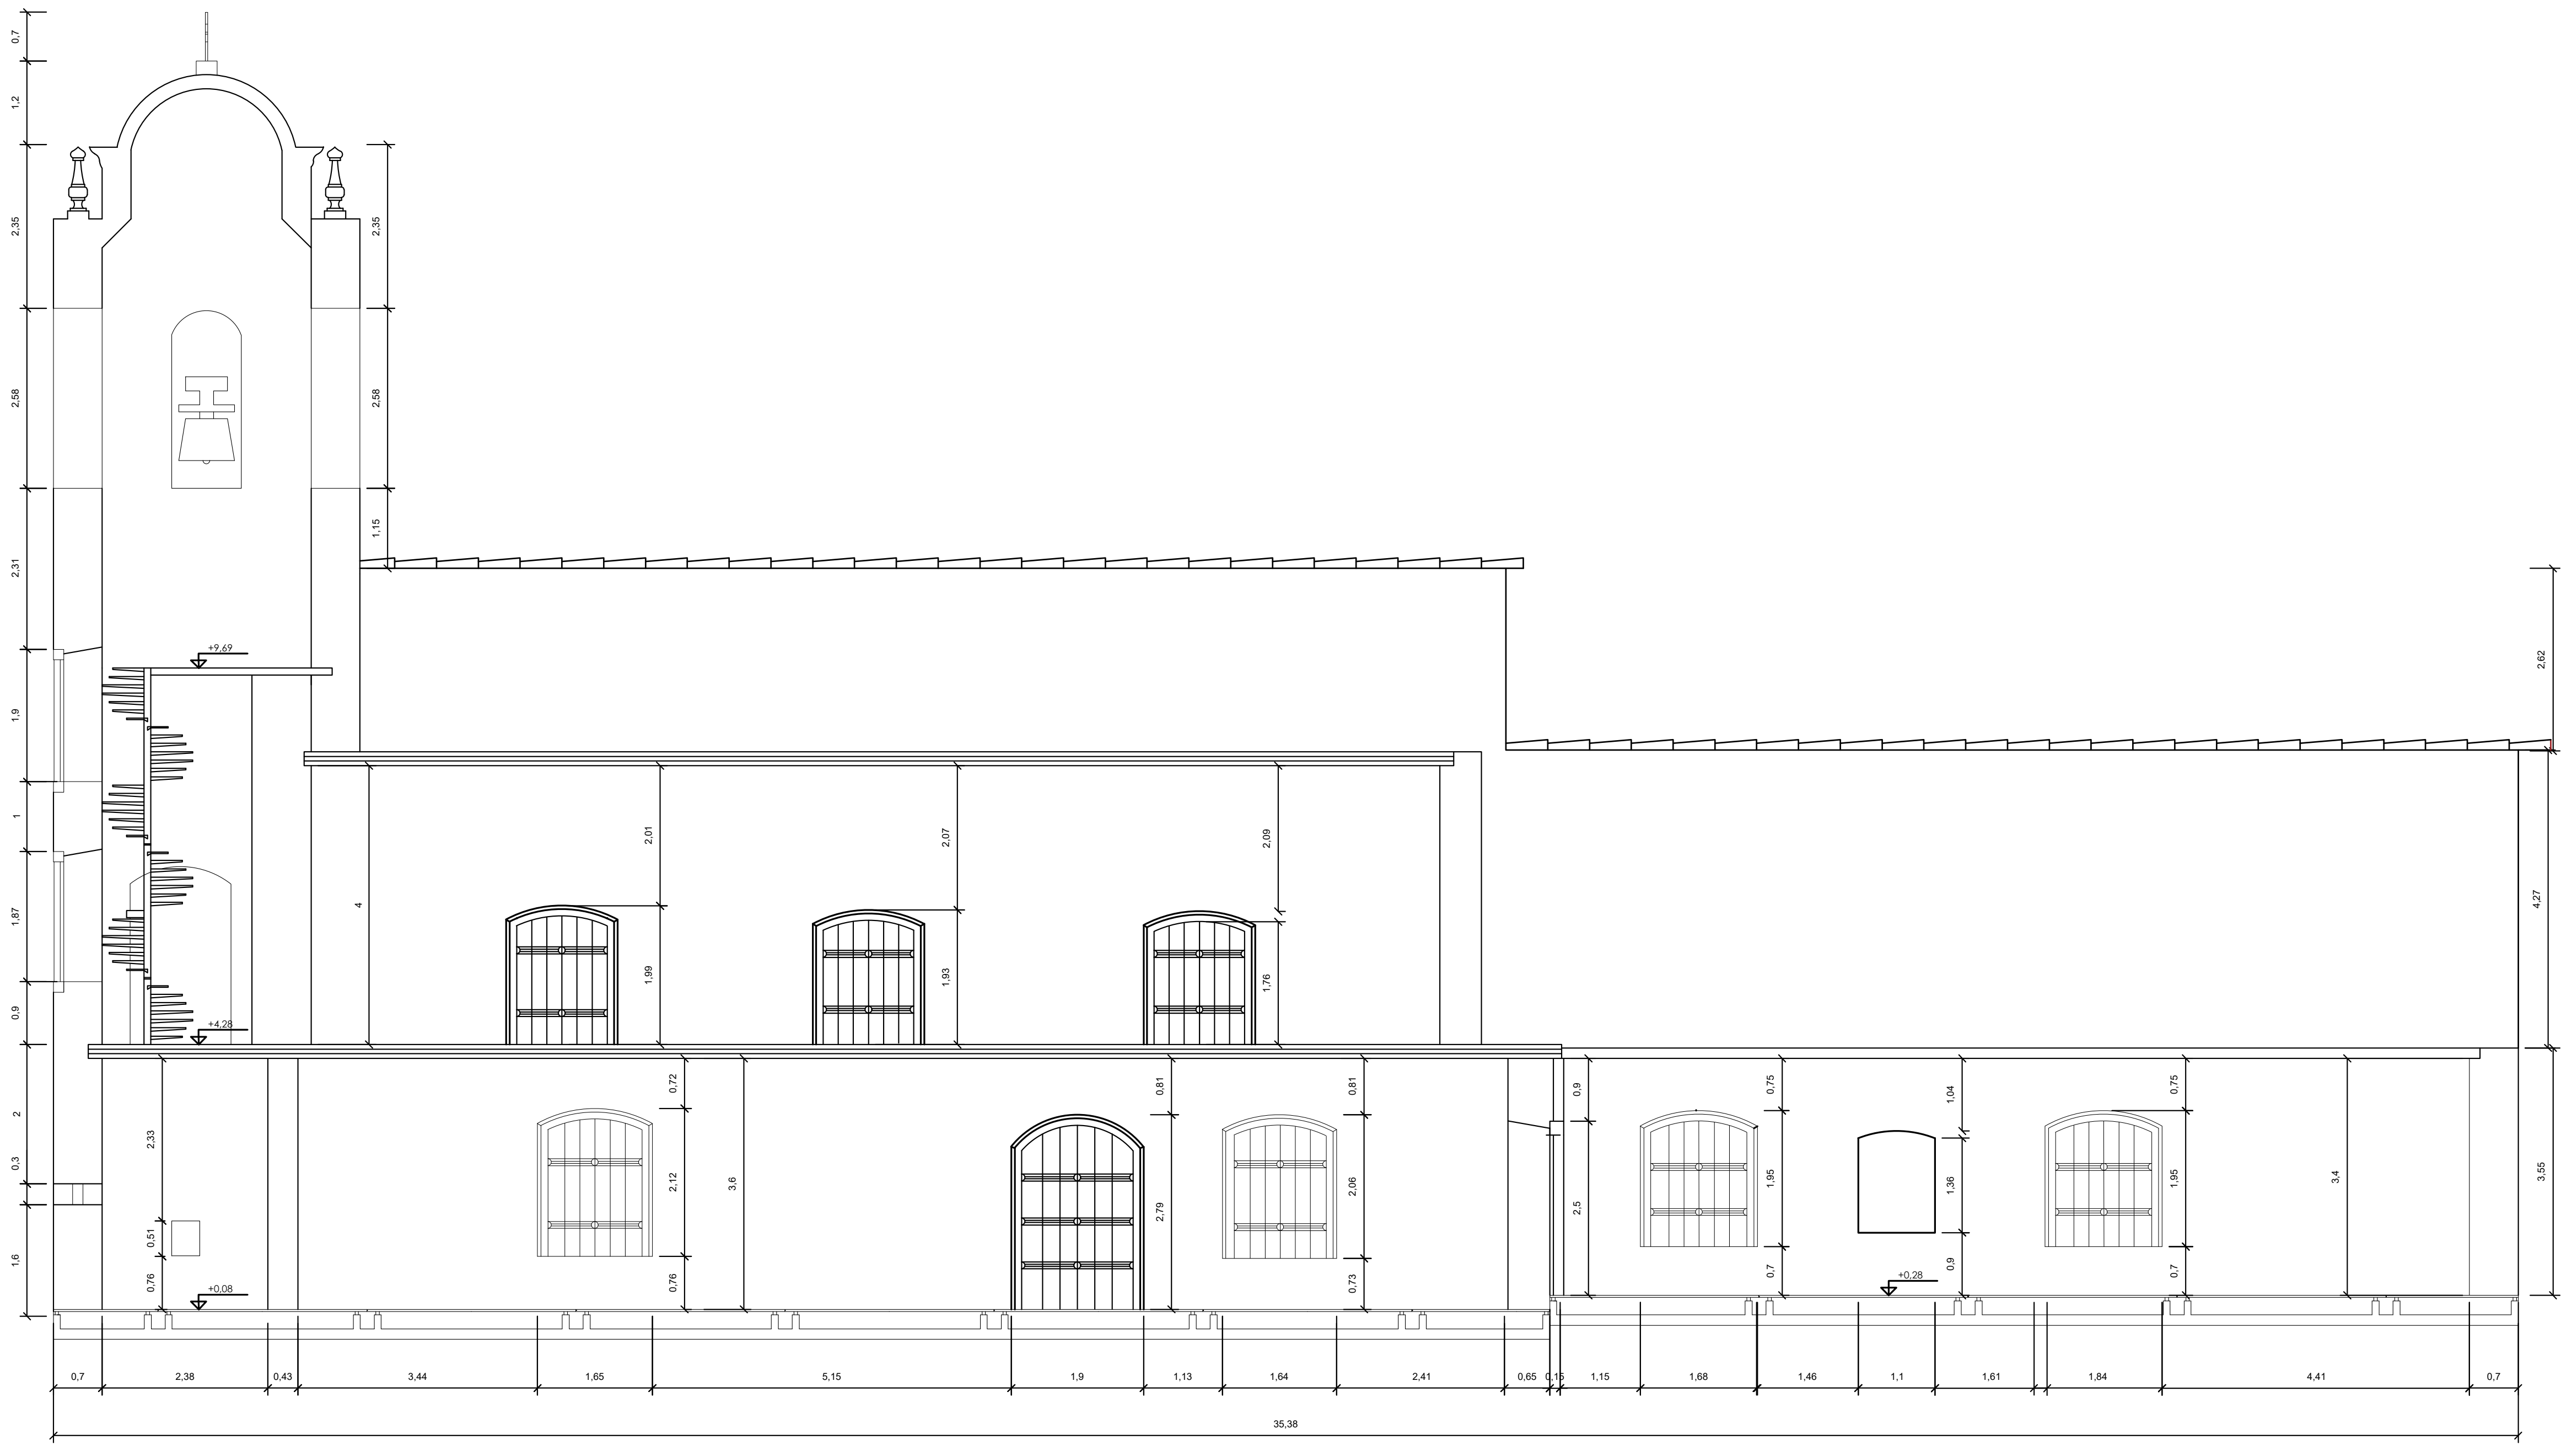
0,7
2,38
0,43
3,44
1,65
5,15
1,9
1,13
1,64
2,41
0,65
0,15
1,15
1,68
1,46
1,1
1,61
1,84
4,41
0,7
35,38
+0,08
+0,28

CORTE DD

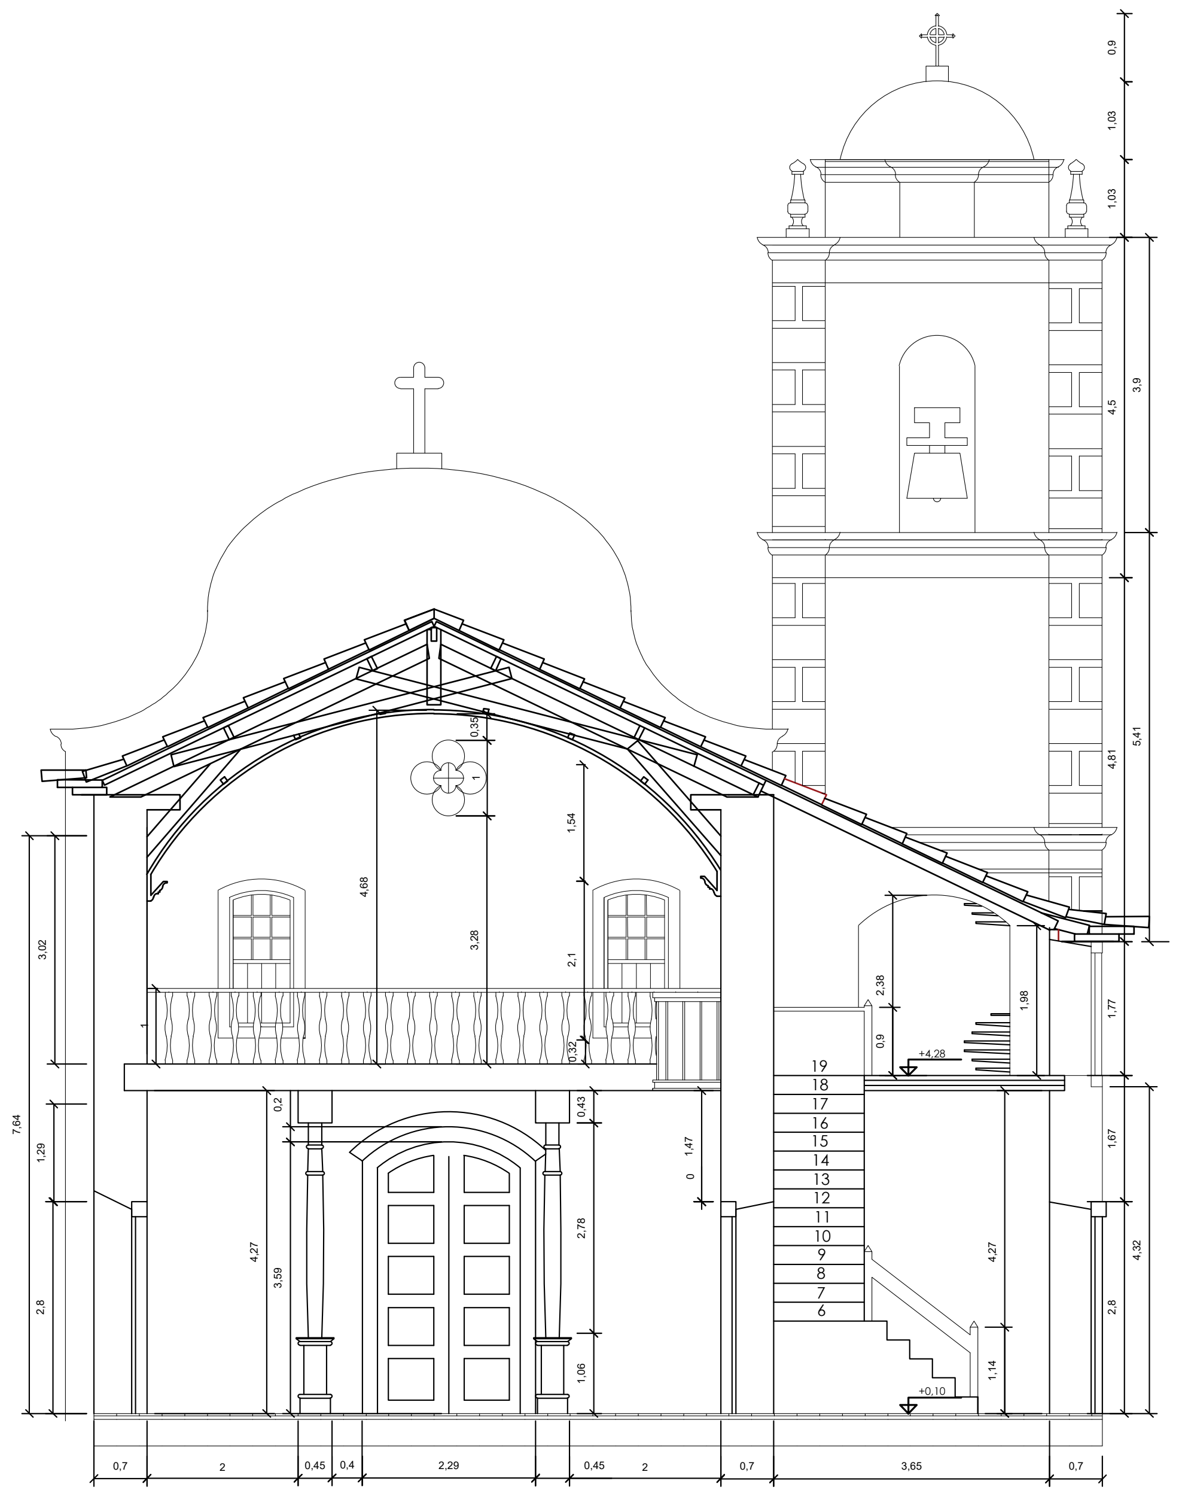

CORTE EE

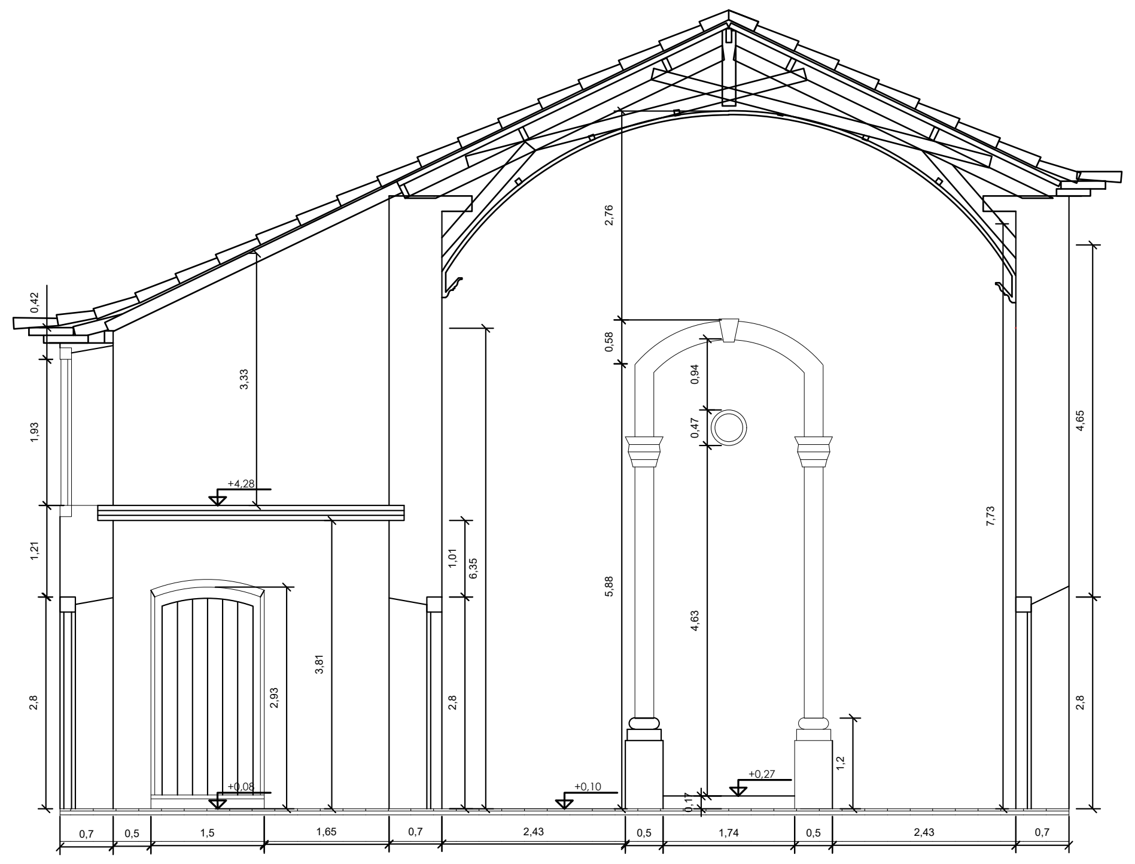

CORTE FF

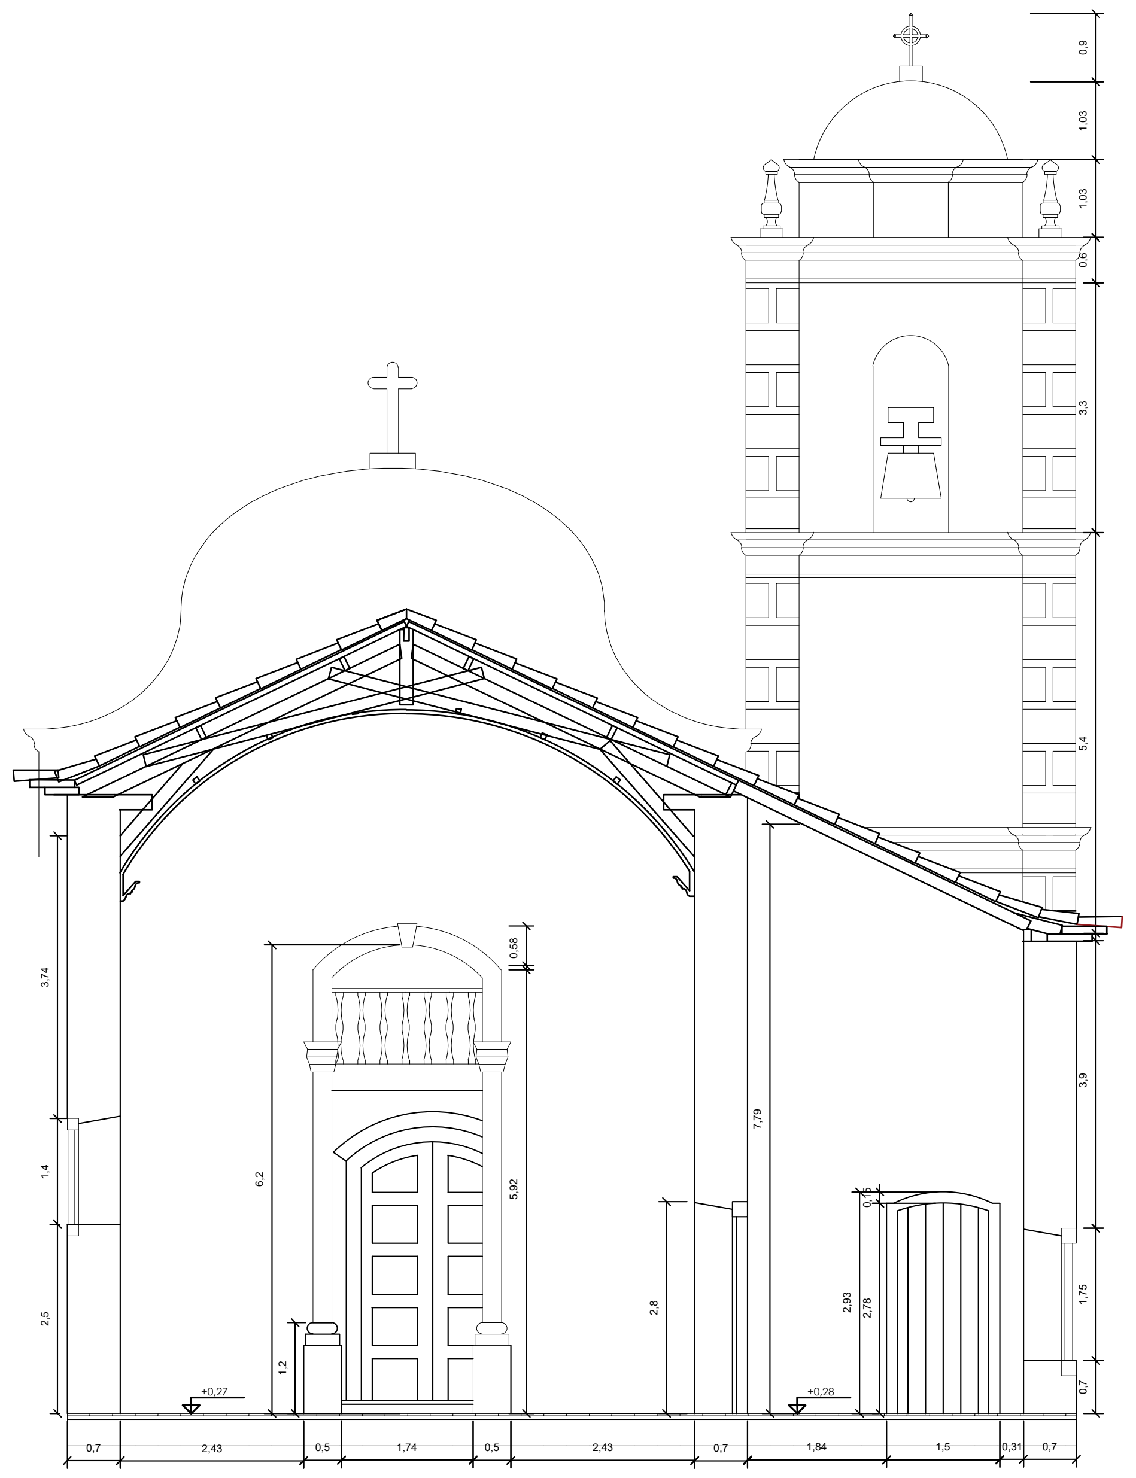

CORTE GG

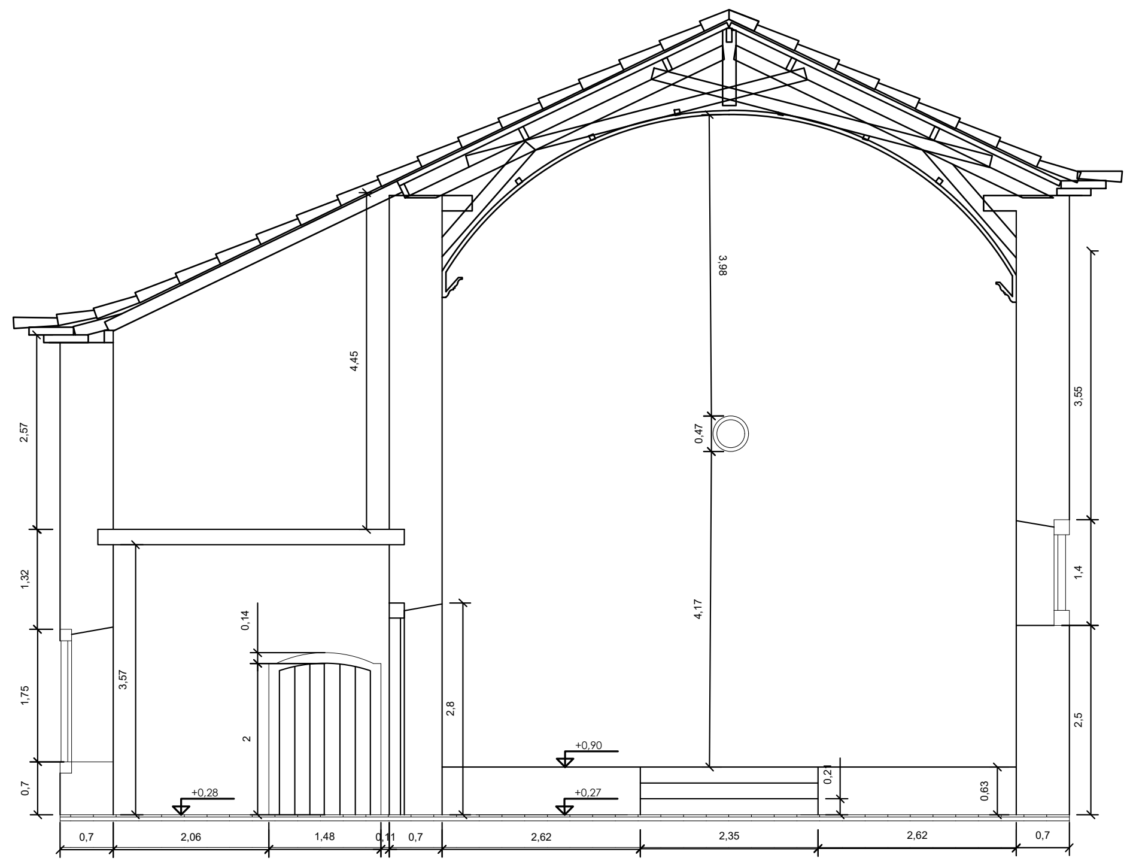

CORTE HH

PROJETO ARQUITETÔNICO

LEI COMPLEMENTAR Nº 84 DE 1993

FOLHA: Nº 4/5

ESCALA: 1:100

ASSUNTO: PROJETO DE PAVIMENTOS E COBERTURA

LOCAL: PRAÇA NARCISO DE ANDRADE, S/N
- CENTRO HISTÓRICO, ITANHAÉM / SP

PROP. MITRA DIOCESANA DE SANTOS
MATRIZ DE SANT'ANNA DE ITANHAÉM

SITUAÇÃO S/ ESCALA

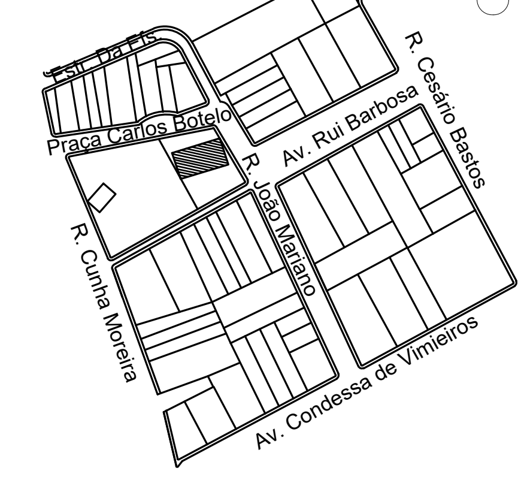
N
Estr. Da Fé
Praça Carlos Botelo
R. João Mariano
Av. Rui Barbosa
R. Cesário Bastos
R. Cunha Moreira
Av. Condessa de Vimieiros

ÁREAS EM M²

TERRENO	1.518
TOTAL CONSTRUÍDO	628,57

AUTOR DO PROJETO E RESP. TÉCNICO
RICARDO ANDALAFT
ARQUITETO E URBANISTA
CAU: A20729-2

ESPAÇO RESERVADO À PREFEITURA MUNICIPAL