
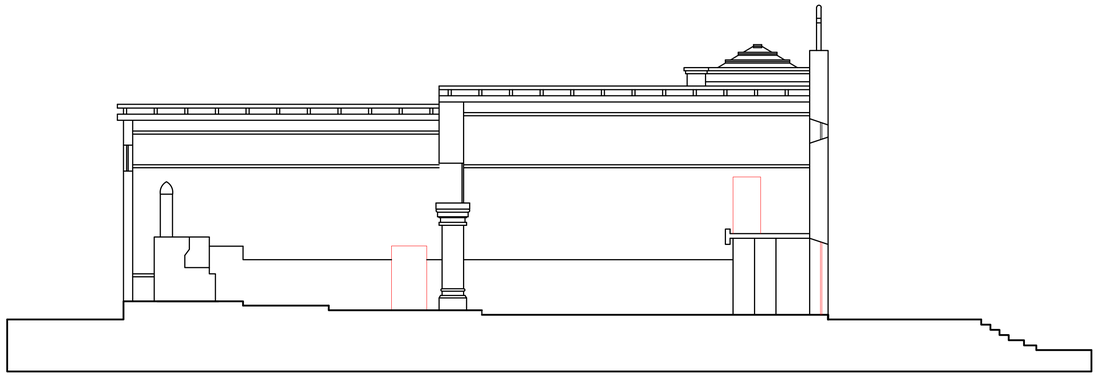


Corte A-A



Imagem 1: Capela do Monte Serrat em 1915 - Foto: álbum Exploração do Litoral - 1ª secção - Cidade de Santos á fronteira do Estado do Rio de Janeiro, da Comissão Geographica e Geológica do Estado de S. Paulo, impresso por Typographia Brazil de Rothschild Co., S. Paulo, 1915. Acesso em 26/02/24

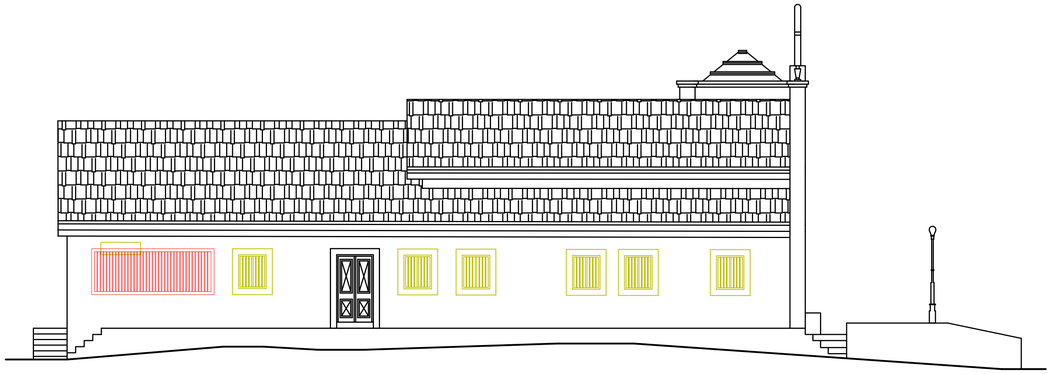

Fachada Sul



Imagem 2: Fachada da edificação. https://40emais.com.br/nossa-senhora-do-monte-serrat/ - acesso em 26/02/24



Fachada Leste

PROJETO ARQUITETÔNICO

LEI COMPLEMENTAR Nº 84 DE 1993

FOLHA: Nº 3/5


ESCALA: 1:100

ASSUNTO: CONSERVAÇÃO E RECUPERAÇÃO DE FACHADA IMÓVEL NP1

LOCAL: CAMINHO MOSENHOR MOREIRA, 33
SANTOS/SP

PROP. MITRA DIOCESANA DE SANTOS
IGREJA DE NOSSA SENHORA DO MONTE SERRAT

SITUAÇÃO S/ ESCALA

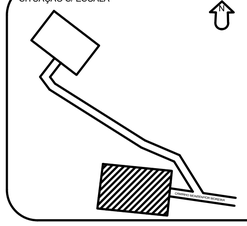

ÁREAS EM M²

TERRENO 547,11

TOTAL CONSTRUÍDO 547,11

MITRA DIOCESANA DE SANTOS

AUTOR DO PROJETO E RESP. TÉCNICO
RICARDO ANDALAFT
ARQUITETO E URBANISTA
CAU: A20729-2

ESPAÇO RESERVADO A PREFEITURA MUNICIPAL