



Planta de Cobertura | Esc. 1:150

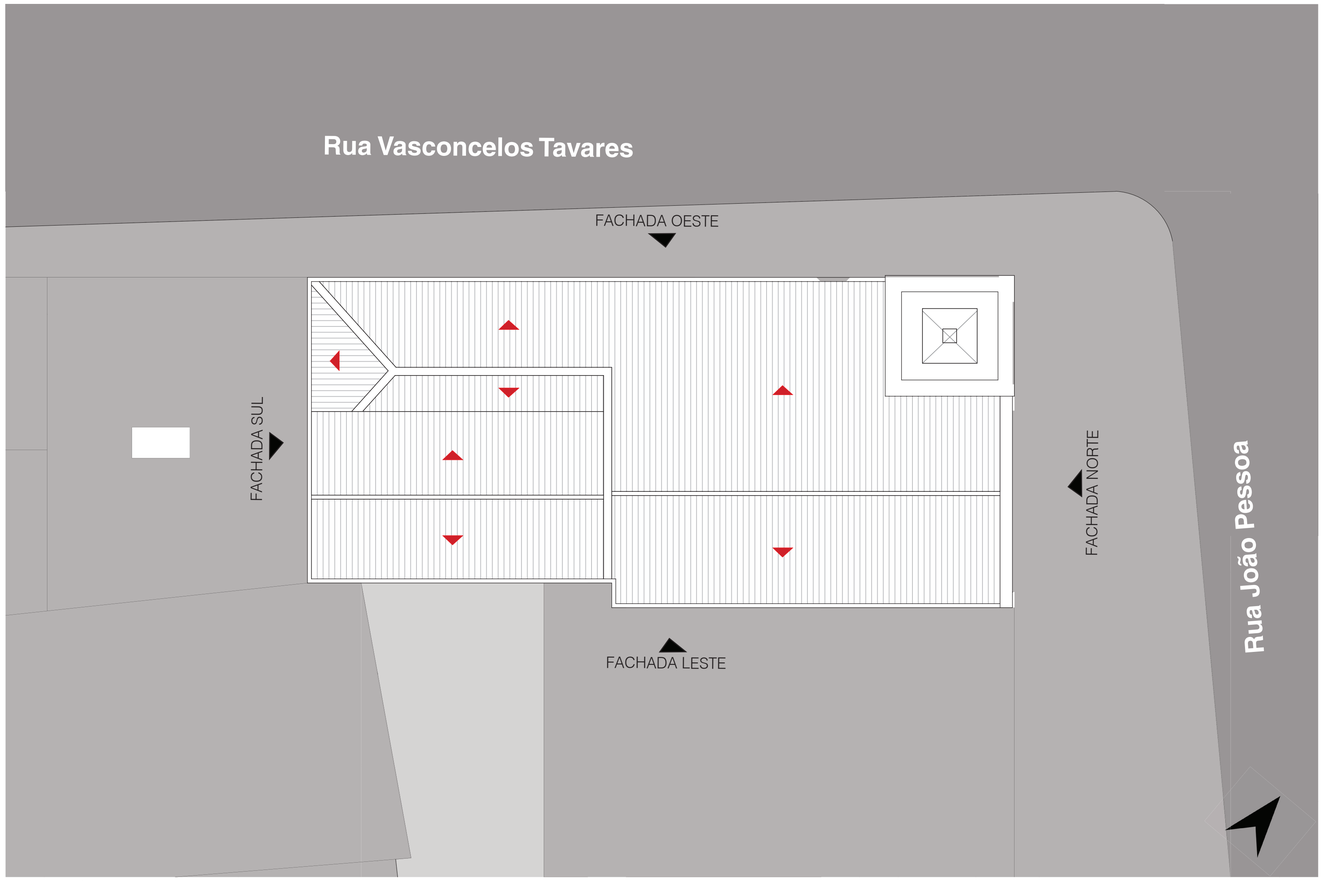

Planta de Situação | Lote Igreja Nossa Senhora do Rosário destacado | Esc. 1:250

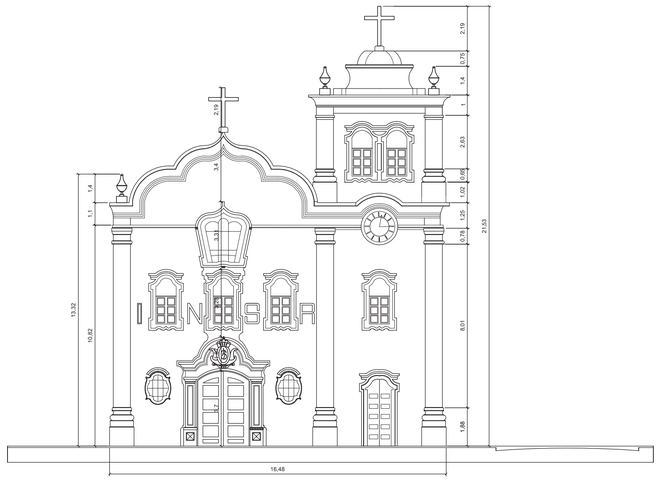

Fachada Norte | Esc. 1:150



Fachada Oeste| Esc. 1:150


achtt
ARCHITETANDO

PROJETO ARQUITETÔNICO
LEI COMPLEMENTAR Nº 84 DE 1993

FOLHA: Nº 1/4
ESCALA: indicada

ASSUNTO: CONSERVAÇÃO E RECUPERAÇÃO DE FACHADA IMÓVEL NP1
LEVANTAMENTO DE PATOLOGIAS
LOCAL: PRAÇA RUY BARBOSA, S/N, CENTRO
SANTOS/SP
PROP. MITRA DIOCESANA DE SANTOS
IGREJA DE NOSSA SENHORA DO ROSÁRIO

SITUAÇÃO S/ ESCALA

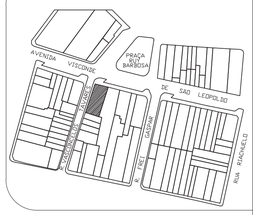


ÁREAS EM M²

TERRENO	560,00
TOTAL CONSTRUÍDO	1198,60

AUTOR DO PROJETO E RESP. TÉCNICO
RICARDO ANDALAFT
ARQUITETO E URBANISTA
CAU: A20729-2


ESPAÇO RESERVADO À PREFEITURA MUNICIPAL

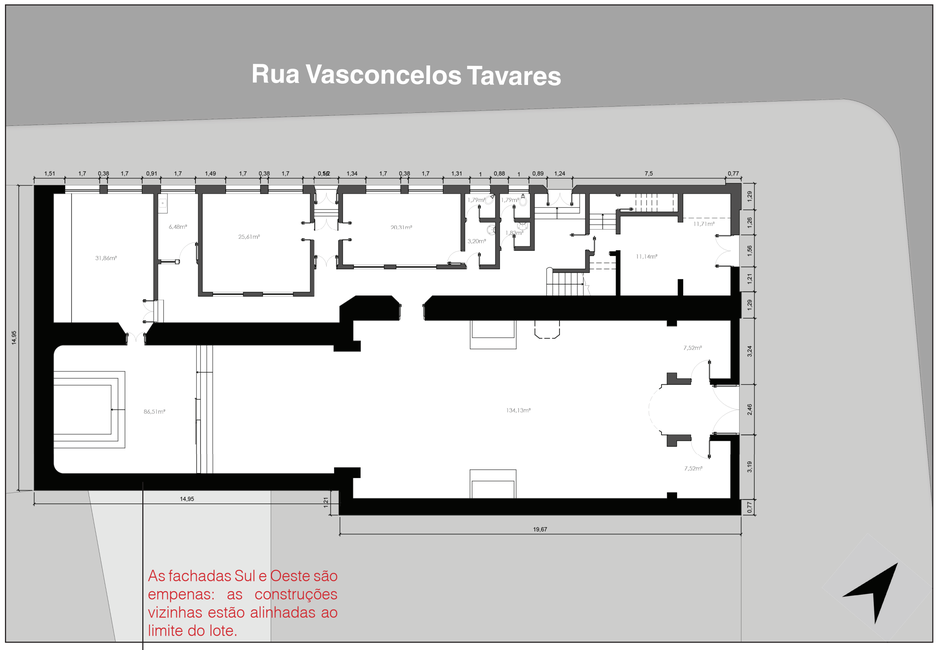

Planta Baixa - Térreo | Esc. 1:150

LEGENDA


- Estrutura em pedra
- Alvenaria

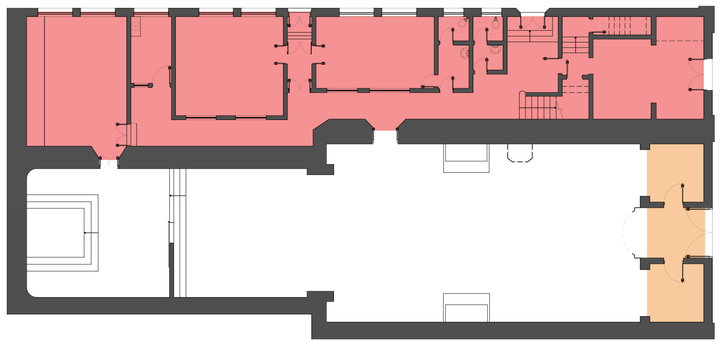


Planta Esquemática | Cronologia Arquitetônica | Esc. 1:50

LEGENDA


- Remanescente do original de 1822 com alvenaria de pedra
- Fachadas e coros construídos em 1935, resultado do alargamento da Praça Rui Barbosa, com alvenaria de tijolos e estrutura em concreto armado
- Construção de 1944 e anexos com alvenaria de tijolos e estrutura em concreto armado

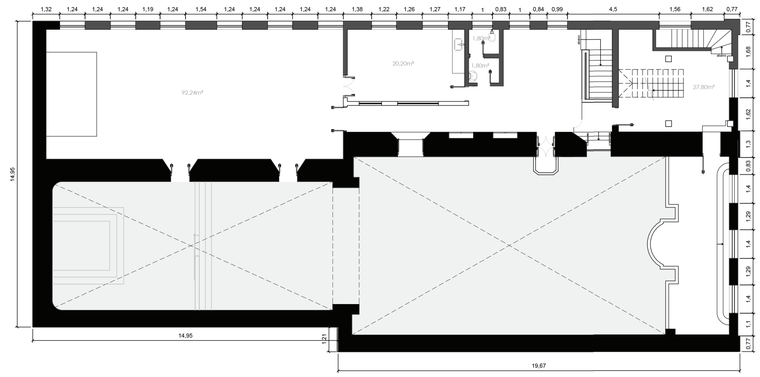

Planta Baixa - 1º Pavimento| Esc. 1:150

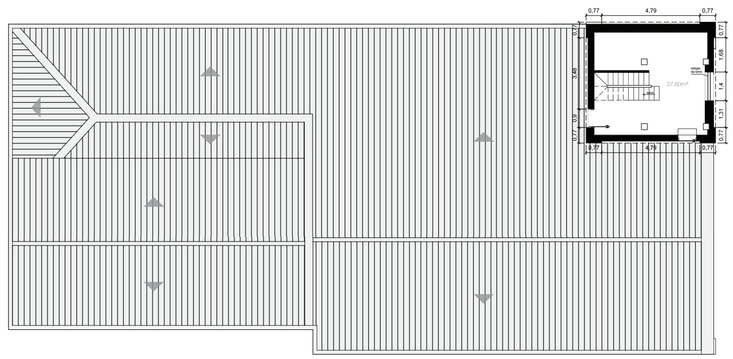

Planta Baixa - 2º Pavimento | Torre | Esc. 1:150

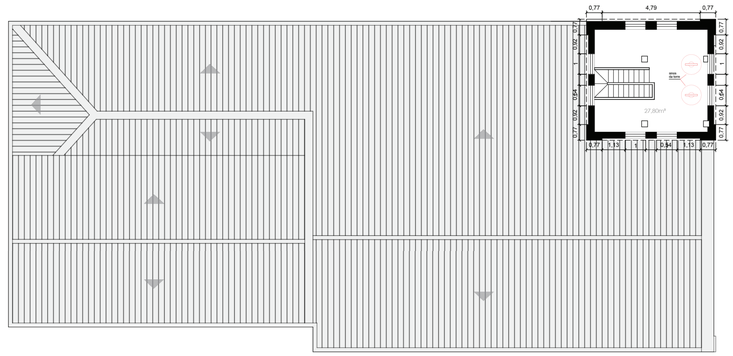

Planta Baixa - 3º Pavimento | Torre |Esc. 1:150

aChtt ARCHITETANDO

PROJETO ARQUITETÔNICO

LEI COMPLEMENTAR Nº 84 DE 1993

FOLHA: Nº 2/4


ESCALA: indicada

ASSUNTO: CONSERVAÇÃO E RECUPERAÇÃO DE FACHADA IMÓVEL NP1
LEVANTAMENTO DE PATOLOGIAS

LOCAL: PRAÇA RUY BARBOSA, S/N, CENTRO
SANTOS/SP

PROP. MITRA DIOCESANA DE SANTOS
IGREJA DE NOSSA SENHORA DO ROSÁRIO

SITUAÇÃO S/ ESCALA

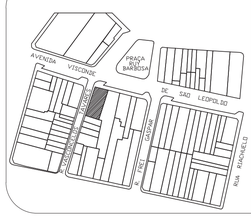


ÁREAS EM M²


TERRENO	560,00
TOTAL CONSTRUÍDO	1198,60

AUTOR DO PROJETO E RESP. TÉCNICO
RICARDO ANDALAFT
ARQUITETO E URBANISTA
CAU: A20729-2

ESPAÇO RESERVADO À PREFEITURA MUNICIPAL

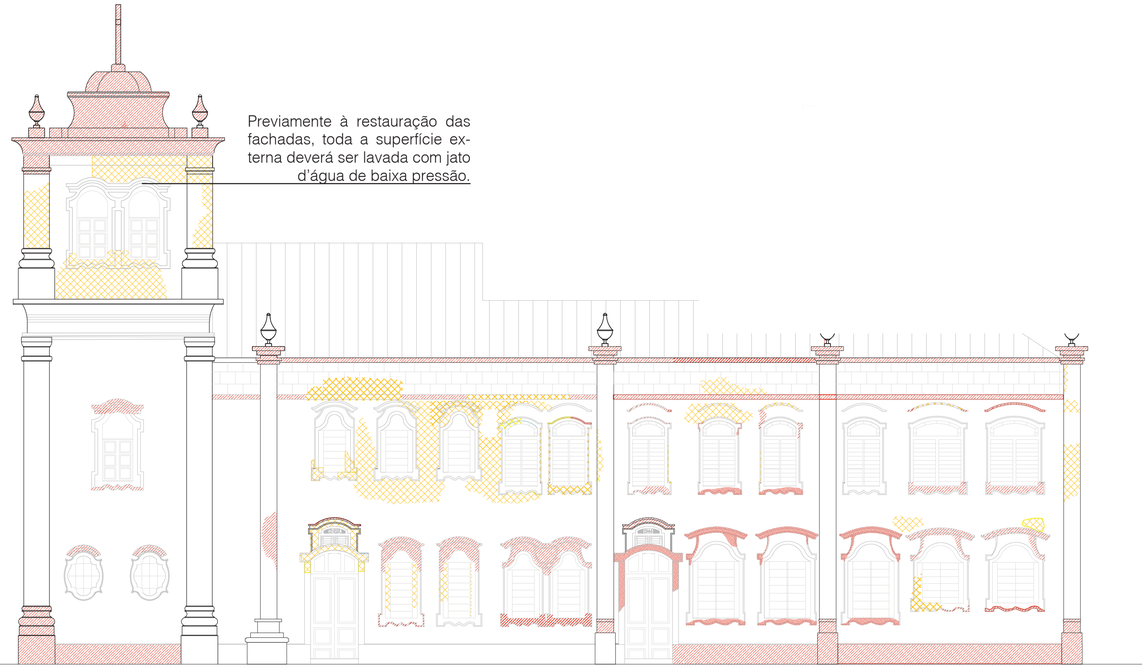

Fachada Oeste | Mapeamento de danos |Esc. 1:100

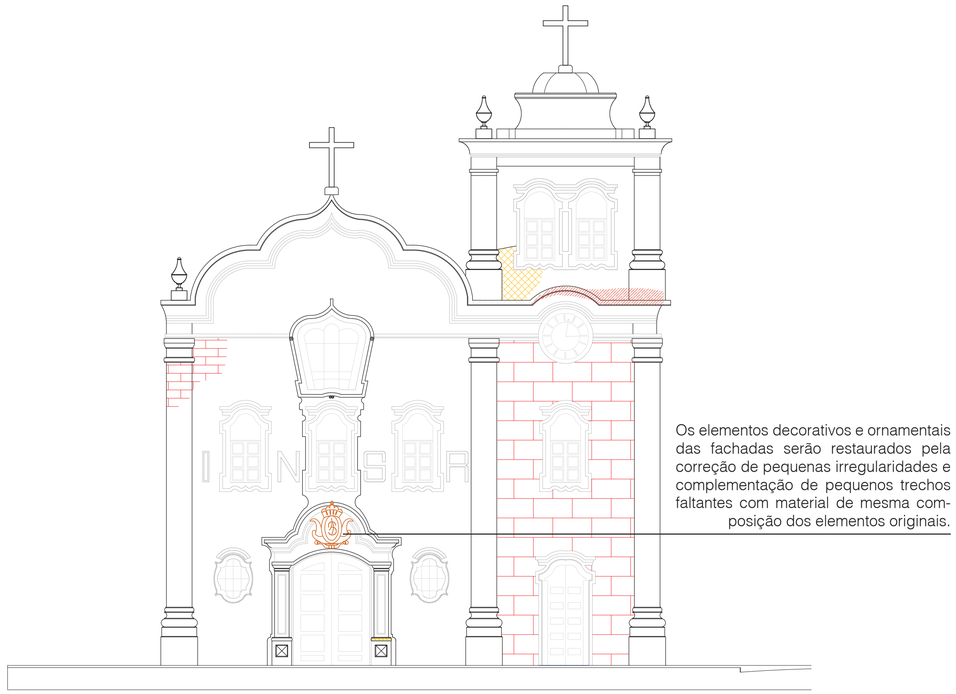

Fachada Norte | Mapeamento de danos |Esc. 1:100

LEGENDA DAS PATOLOGIAS

- SUJIDADE*
- VEGETAÇÃO
- DESPLACAMENTO
- INTERVENÇÕES INDEVIDAS
- UMIDADE**

* Devido a falta de manutenção do imóvel, podemos considerar a presença de sujidade em sua área total dos fachadas.

** Umidade acumulada em todos os relevos do edificação, fato natural em construções desse tipo.


Informações complementares:

Localização específica de desplacamento de massa raspada em grid:




LEGENDA PATOLOGIA

- DESPLACAMENTO

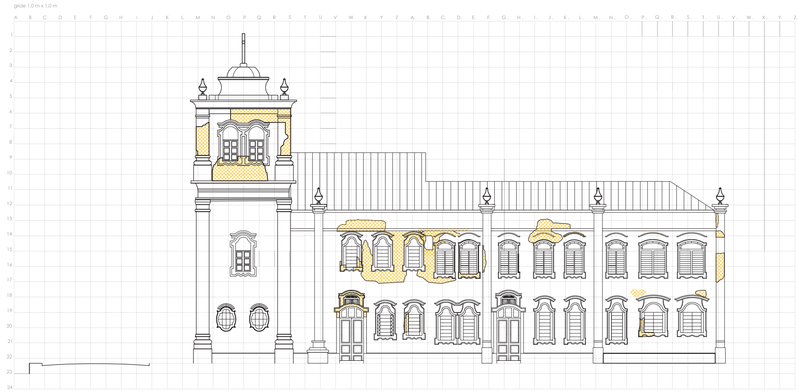

Planta de localização de andaimes para execução de obra

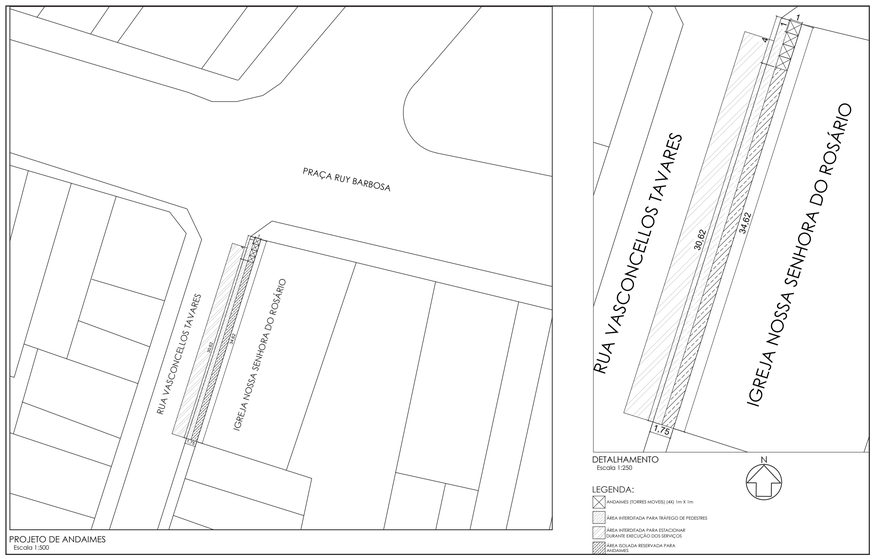

Obs.: O detalhamento de patologias mapeadas encontra-se no Memorial Descritivo deste projeto.

achtt ARCHITETANDO

PROJETO ARQUITETÔNICO

LEI COMPLEMENTAR Nº 84 DE 1993

FOLHA: Nº 3/4


ESCALA: indicada

ASSUNTO: CONSERVAÇÃO E RECUPERAÇÃO DE FACHADA IMÓVEL NP1
LEVANTAMENTO DE PATOLOGIAS

LOCAL: PRAÇA RUY BARBOSA, S/N, CENTRO
SANTOS/SP

PROP. MITRA DIOCESANA DE SANTOS
IGREJA DE NOSSA SENHORA DO ROSÁRIO

SITUAÇÃO S/ ESCALA

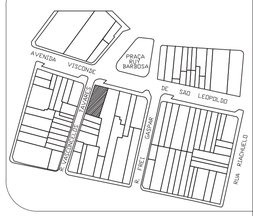


ÁREAS EM M²


TERRENO	560,00
TOTAL CONSTRUÍDO	1198,60

AUTOR DO PROJETO E RESP. TÉCNICO
RICARDO ANDALAFT
ARQUITETO E URBANISTA
CAU: A20729-2

ESPAÇO RESERVADO À PREFEITURA MUNICIPAL

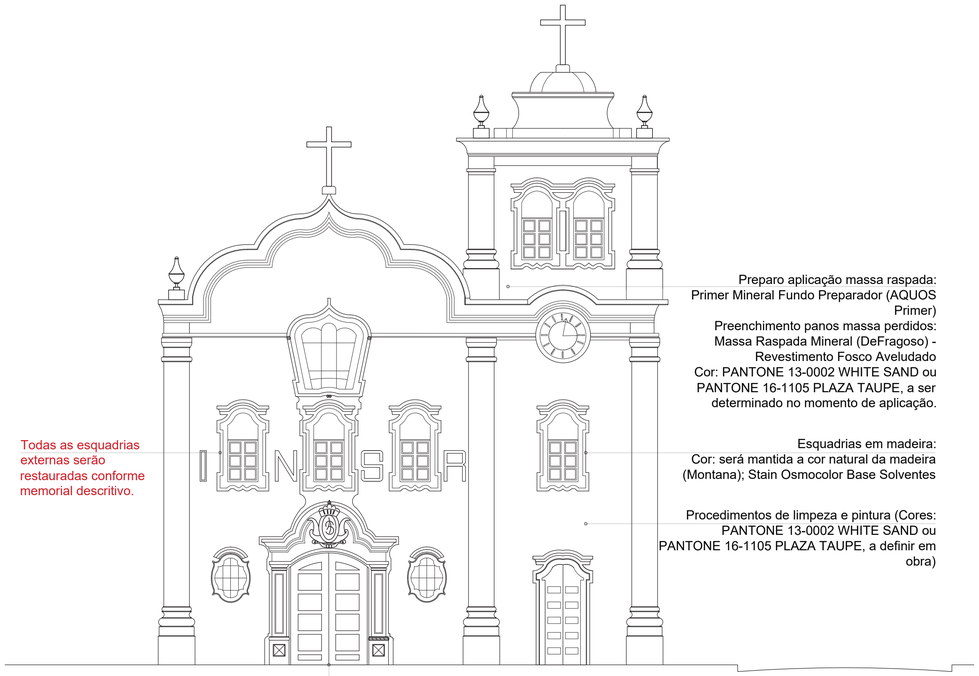

Fachada Norte| Restauração |Esc. 1:100

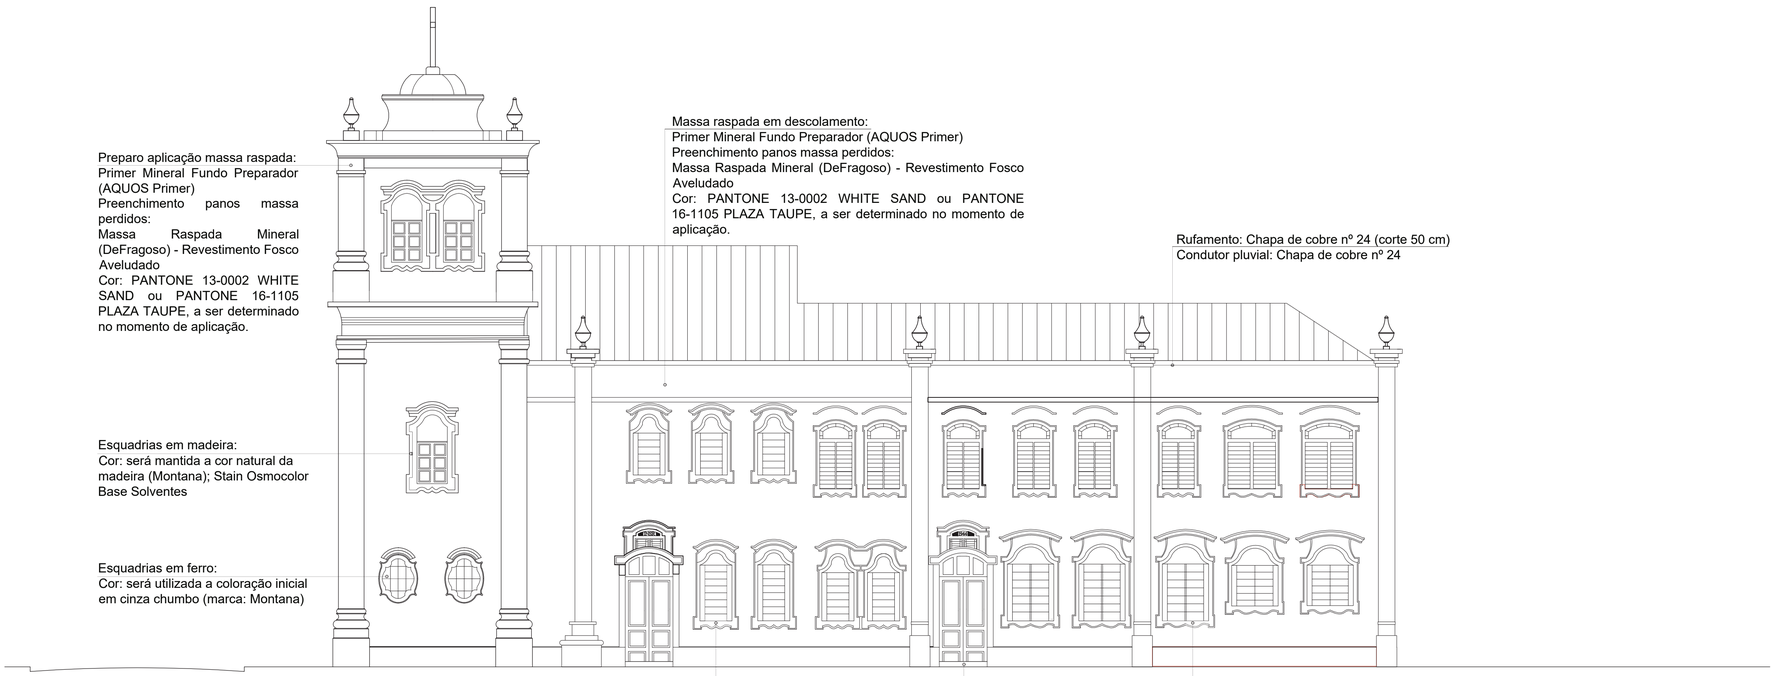

Fachada Oeste | Restauração |Esc. 1:100



Vistas 3D | Situação

aChtt
ARCHITETANDO

PROJETO ARQUITETÔNICO

LEI COMPLEMENTAR Nº 84 DE 1993

FOLHA: Nº 4/4


ESCALA: indicada

ASSUNTO: CONSERVAÇÃO E RECUPERAÇÃO DE FACHADA IMÓVEL NP1
LEVANTAMENTO DE PATOLOGIAS

LOCAL: PRAÇA RUY BARBOSA, S/N, CENTRO
SANTOS/SP

PROP. MITRA DIOCESANA DE SANTOS
IGREJA DE NOSSA SENHORA DO ROSÁRIO

SITUAÇÃO S/ ESCALA

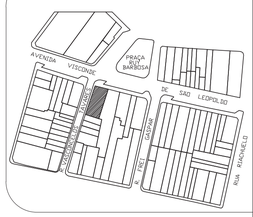

ÁREAS EM M²

TERRENO	560,00
TOTAL CONSTRUÍDO	1198,60

AUTOR DO PROJETO E RESP. TÉCNICO
RICARDO ANDALAFT
ARQUITETO E URBANISTA
CAU: A20729-2

ESPAÇO RESERVADO À PREFEITURA MUNICIPAL